
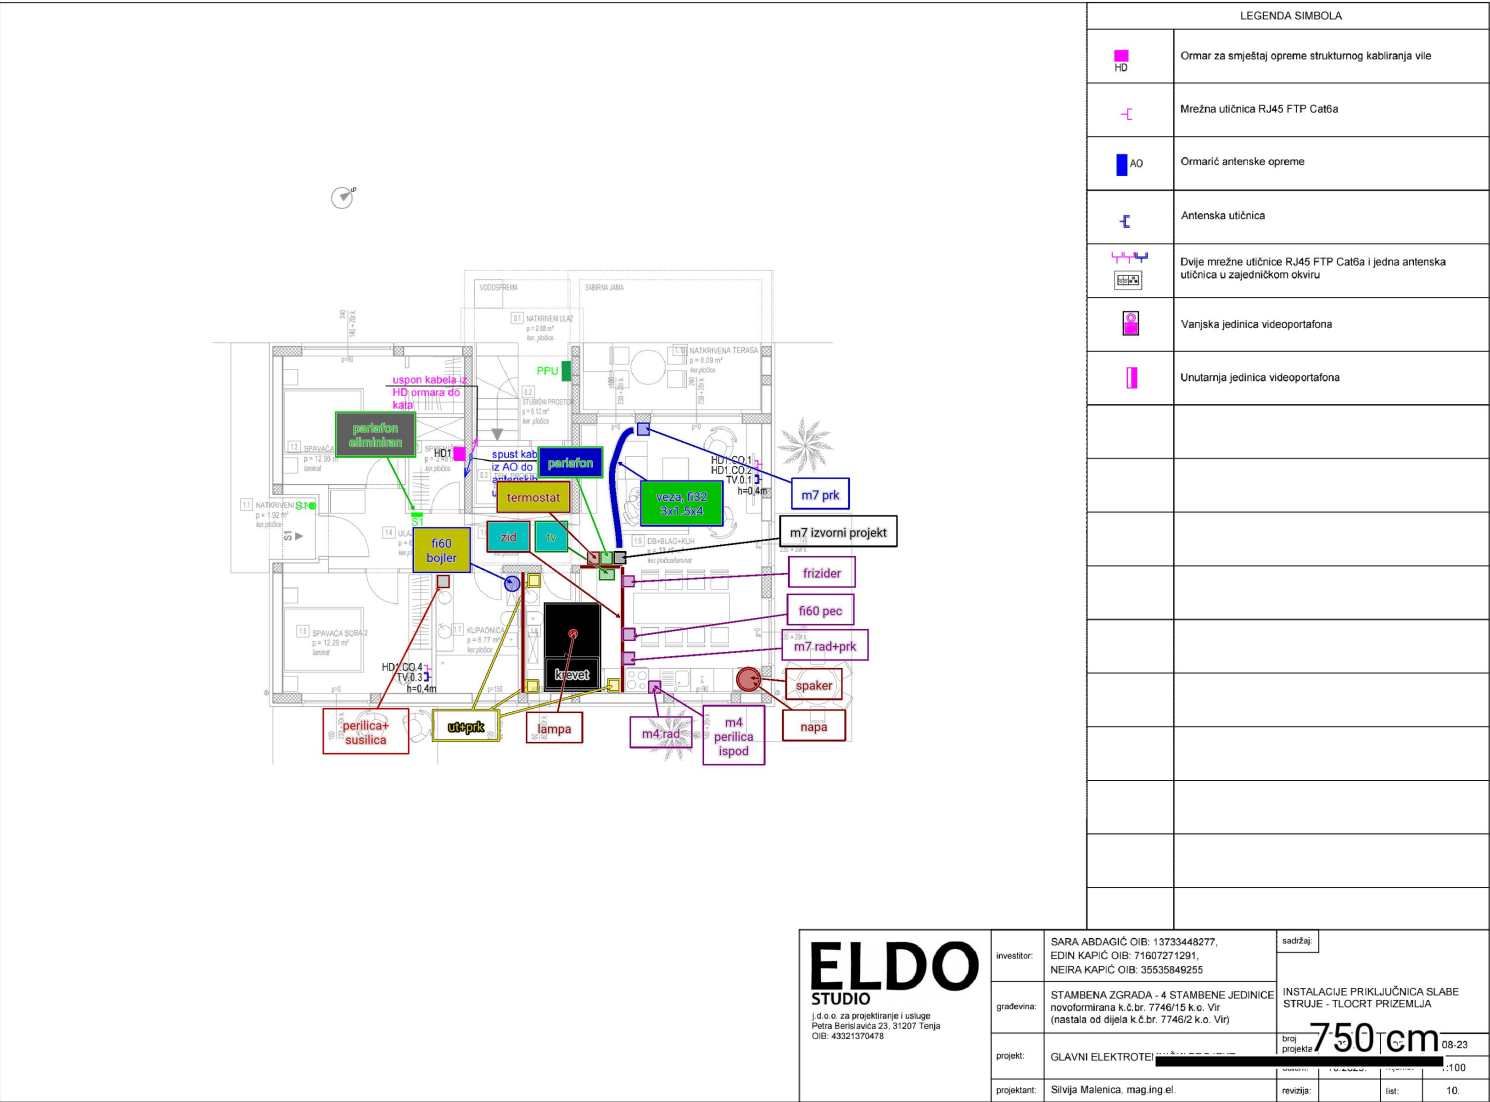
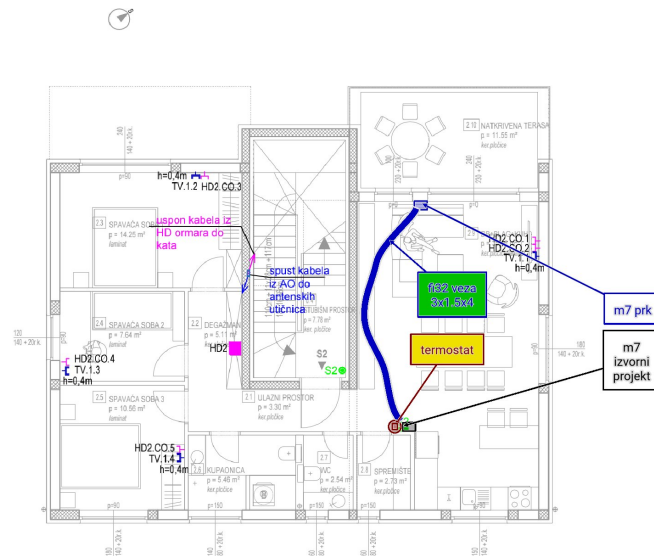


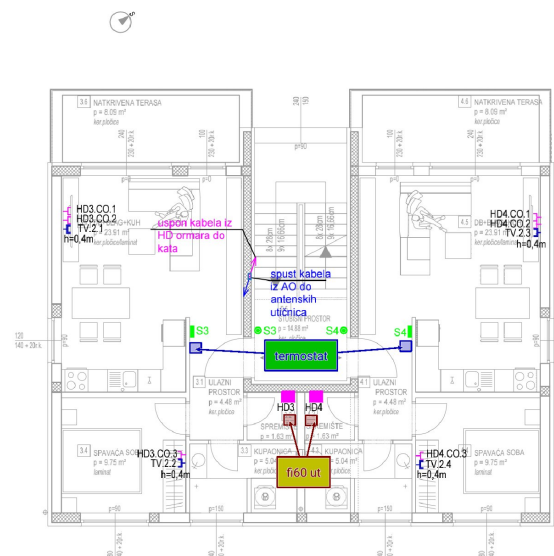


1.kat.promjene

[illegible]

 d.o.o. za projektiranje i usluge Pula, Brestova 23a, 31207 Tinja e-mail: 433213074@el.fo	investitor:	SARA ABDAGIĆ OIB: 137353448277, EDIN KAPIC OIB: 71807271291, NEIRA KAPIC OIB: 35535849255	saobraz:	
	građevina:	STAMBENA ZGRADA - 4 STAMBENE JEDINICE novogradnja k.č.br. 774615 s k.o. Vje (nastavi od dijela k.č.br. 77462 k.o. Vin)	INSTALACIJE PRIKLJUČNICA SLABE STRUJE - TLOCRT 1. KATA	
	projekt:	GLAVNI ELEKTROTEHNIČKI PROJEKT	broj projekta:	23-06 ZOP: 08-23
	projektant:	Silvija Malenica, mag.ing. el.	datum:	10. 2023. mjenio: 1:1:00
			revizija:	list: 11

[illegible]

ELDO STUDIO i.d.o.o. za projektiranje i usluge Petra Baranovića 28, 31207 Tinja HR: 43321370478	investitor:	SARA ABDAGIĆ i.d.o.o.: 13733448277, EDIN KAPIC i.d.o.o.: 71607271291, NEIRA KAPIC i.d.o.o.: 35535849255	sadržaj:	
	građevina:	STAMBENA ZGRADA, 4 STAMBENE JEDINICE novoliformirane k.c.b.r. 7746/15 k.c. Vir (nastala od dijela k.c.b.r. 7746/2 k.o. Vir)	broj projekta	7501cm-06-23
projekt:	GLAVNI ELEKTROTEHNIČAR: [REDACTED]		revizija:	1:100
projektant:	Silvija Malenica, mag.ing.el.		list:	12.

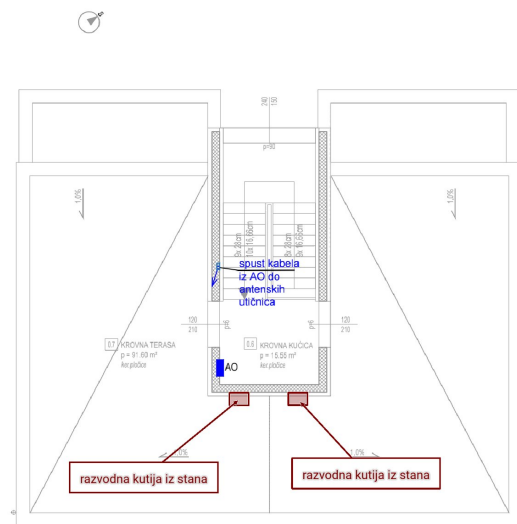[illegible]

 ELDO STUDIO J.d.o.o. za projektiranje i usluge Petra Benkovića 23, 31207 Tinja e-mail: 4332137047a	investitor:	SARA ABDAGIĆ OIB: 13733448277, EDIN KAPIĆ OIB: 7160721291, NEIRA KAPIĆ OIB: 35535849255	sažetak:			
	građevina:	STAMBENA ZGRADA - 4 STAMBENE JEDINICE novodimenzirana k.c.br. 77462/15 s.o. Vir (nastala od dijela k.c.br. 77462/2 s.o. Vir)	INSTALACIJE PRIKLJUČNICA SLABE STRUJE - TLOCRT KROVA			
	projekt:	GLAVNI ELEKTROTEHNIČKI PROJEKT	broj projekta:	23-06	ZOP:	08-23
			datum:	10. 2023.	mirno:	1:100
	projektant:	Silvija Malenica, mag.ing.el.	revizija:			13